

SAND CREEK ESTATES DIVISION No. 2

A SUBDIVISION OF THE CITY OF IDAHO FALLS, BONNEVILLE COUNTY, IDAHO
BEING PART OF THE NORTHWEST 1/4 OF SECTION 4,
TOWNSHIP 1 NORTH, RANGE 38 EAST OF THE BOISE MERIDIAN





NORTHWEST CORNER OF SECTION 4,
FOUND BRASS CAP MONUMENT
PURSUANT TO CP&F INSTRUMENT No. 1725834

CANAL RIGHT-OF-WAY

ALL CANALS, AS SHOWN HEREON, EXIST WITHIN A RIGHT-OF-WAY DEFINED BY I.C. 542-1102 AND MUST HAVE WRITTEN PERMISSION OF THE OWNER OR OPERATOR OF THE RIGHT-OF-WAY TO CONSTRUCT ANYTHING WITHIN, UNDER, UPON OR OVER THE AREA, TO ENSURE THAT ANY SUCH ENCROACHMENTS WILL NOT UNREASONABLY OR MATERIALLY INTERFERE WITH THE USE AND ENJOYMENT OF THE RIGHT-OF-WAY.

SHELDON DANCE AND PAT DANCE
DEED INSTRUMENT No. 1523269
NOT PLATTED

SHELDON R. DANCE AND PATRICIA T. DANCE
DEED INSTRUMENT No. 1247752
NOT PLATTED

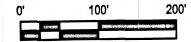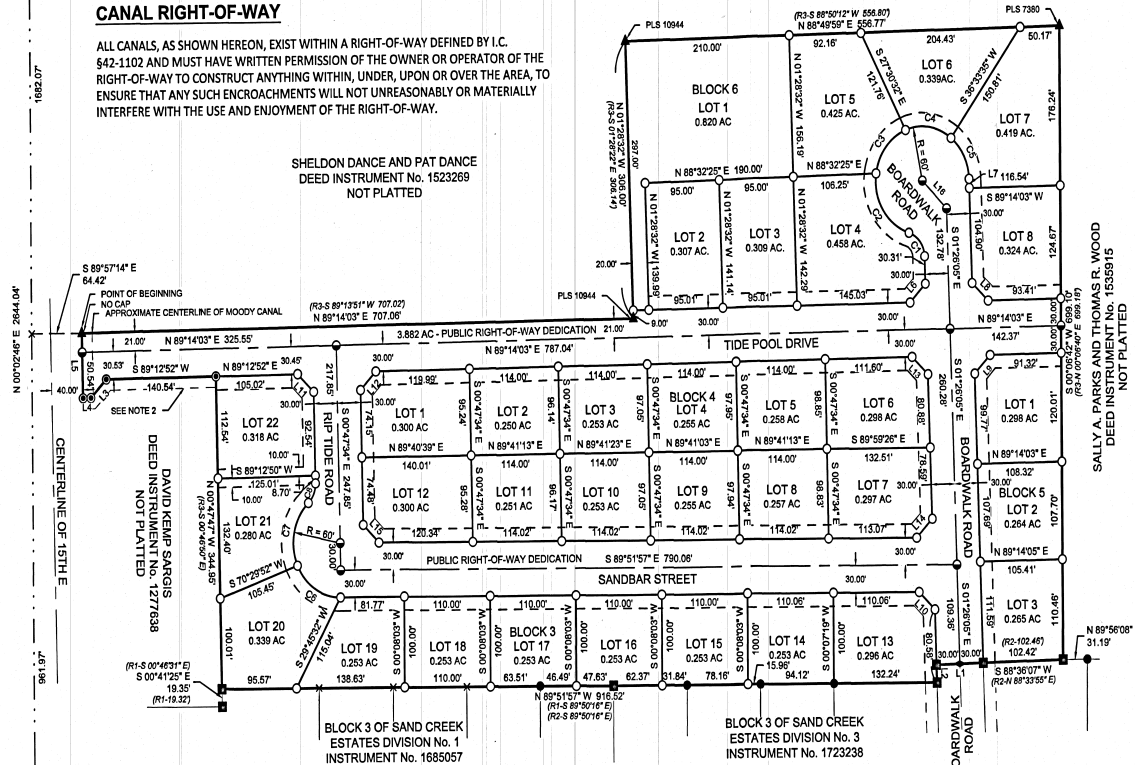

LEGEND

- PLSS SECTION CORNER AS NOTED
- PLSS QUARTER CORNER AS NOTED
- FOUND ALUMINUM CAP MONUMENT STAMPED "PLS 14222"
- FOUND 5/8" REBAR WITH PLASTIC CAP STAMPED "PLS 14222"
- FOUND 1/2" REBAR WITH PLASTIC CAP STAMPED "PLS 14222"
- FOUND 1/2" REBAR AS NOTED, REPLACED WITH 5/8" REBAR WITH PLASTIC CAP STAMPED "PLS 18405"
- SET 5/8" REBAR WITH PLASTIC CAP STAMPED "PLS 18405"
- SET 5/8" REBAR WITH ALUMINUM CAP STAMPED "PLS 18405"
- SET 1/2" REBAR WITH PLASTIC CAP STAMPED "PLS 18405"
- CALCULATED POINT (NOTHING FOUND, NOTHING SET)
- SUBDIVISION BOUNDARY
- SECTION LINE
- LOT LINE
- PUBLIC UTILITY EASEMENT (PUE)
- DIMENSIONAL TIE LINE
- ADJOINING PARCELS
- PUBLIC STREET CENTERLINE
- EXISTING EASEMENT AS NOTED
- SAND CREEK ESTATES DIVISION No. 1 INSTRUMENT No. 1685057
- SAND CREEK ESTATES DIVISION No. 3 INSTRUMENT No. 1723238
- RECORD OF SURVEY INSTRUMENT No. 1541216

SURVEY NARRATIVE

THIS SURVEY WAS MADE AT THE REQUEST OF HF VENTURES, LLC TO CREATE LOTS, BLOCKS AND STREETS.

THE SOUTH BOUNDARY WAS DETERMINED BY FOUND MONUMENTS AND RECORD INFORMATION FROM SAND CREEK ESTATES DIVISION No. 1 AND No. 3 FILED UNDER INSTRUMENT No. 1685057 AND No. 1723238. THE WEST, NORTH AND EAST BOUNDARIES WERE DETERMINED BY FOUND MONUMENTS AND RECORD INFORMATION FROM RECORD OF SURVEY INSTRUMENT No. 1541216. ADJOINING DEED INFORMATION AS SHOWN ON THE FACE OF THIS PLAT WAS ALSO USED.

NOTES

- ALL LOT LINES COMMON TO A PUBLIC RIGHT OF WAY HAVE A FIFTEEN FOOT (15') PERMANENT PUBLIC UTILITY EASEMENT.
- 12 FOOT (12') PUBLIC UTILITY EASEMENT PURSUANT TO INSTRUMENT No. 1744540.
- LOT 1 BLOCK 6 IS GRANTED AS A PUBLIC UTILITY AND PUBLIC STORM WATER EASEMENT IN ITS ENTIRETY.

BASIS OF BEARING

ALL MEASURED BEARINGS SHOWN HEREON RELATE DIRECTLY TO THE CITY OF IDAHO FALLS COORDINATE SYSTEM OF 2004, WHICH IS DERIVED FROM THE IDAHO STATE PLANE COORDINATE SYSTEM (EAST ZONE 1101) US SURVEY FEET AND USING A COMBINED SCALE FACTOR OF 1.000277265 FOR A GRID TO GROUND CONVERSION, (REFERENCE FRAME NAD 83(2011), EPOCH 2010.0000). THE SYSTEM ORIENTATION IS BASED ON GRID NORTH ALONG THE EAST ZONE CENTRAL MERIDIAN. NO CONVERGENCE ANGLE HAS BEEN APPLIED.

REFERENCE DOCUMENTS

- CP&F INSTRUMENT No. 16992990
- CP&F INSTRUMENT No. 1725834
- PLAT INSTRUMENT No. 1685057
- PLAT INSTRUMENT No. 1723238
- SURVEY INSTRUMENT No. 1541216
- SURVEY INSTRUMENT No. 1268226
- DEED INSTRUMENT No. 1252388
- DEED INSTRUMENT No. 1667251
- DEED INSTRUMENT No. 1744194
- DEED INSTRUMENT No. 1744195
- DEED INSTRUMENT No. 1758866
- DEEDS SHOWN ON THE FACE OF THIS PLAT

LINE	BEARING	DISTANCE	LINE	BEARING	DISTANCE
L1	S 88°34'00" W	80.00'	(R2-1)	N 89°31'33" E	60.00'
L2	S 01°22'00" E	19.86'	(R2-2)	N 89°31'33" W	20.04'
L3	S 44°13'23" W	28.29'			
L4	S 89°12'52" W	10.00'			
L5	N 00°46'00" W	11.54'			
L6	N 43°33'35" E	28.45'			
L7	S 01°26'00" E	10.00'			
L8	S 46°06'01" E	28.12'			
L9	S 43°53'36" W	28.45'			
L10	N 45°39'01" W	27.89'			
L11	N 45°47'21" W	28.28'			
L12	N 44°12'15" E	26.22'			
L13	S 46°06'01" E	28.12'			
L14	S 44°20'59" W	28.67'			
L15	N 45°19'45" W	28.08'			
L16	S 45°00'00" E	43.53'			

(RECORD INFORMATION LINE TABLE)

LINE	BEARING	DISTANCE
(R2-1)	N 89°31'33" E	60.00'
(R2-2)	N 89°31'33" W	20.04'
(R2-3)	N 89°46'00" W	

CURVE	RADIUS	ARC LENGTH	CHORD LENGTH	CHORD BEARING	DELTA ANGLE
C1	28.00'	34.92'	32.70'	N 37°39'30" W	71°28'49"
C2	60.00'	85.17'	78.20'	N 32°13'01" W	81°19'46"
C3	60.00'	83.73'	80.77'	N 30°36'20" E	80°11'17"
C4	60.00'	81.69'	80.01'	S 81°14'39" E	58°54'25"
C5	60.00'	52.73'	51.05'	S 26°39'48" E	50°21'21"
C6	60.00'	98.44'	95.21'	N 56°57'04" W	63°49'37"
C7	60.00'	72.41'	70.85'	N 11°58'13" E	72°00'46"
C8	28.00'	23.83'	23.12'	N 23°35'31" E	48°46'10"



1823 East Center Street, Pocatello, Idaho 83201 Phone: 208.242.8753
globalandworks@gmail.com globalandworks.com

SAND CREEK ESTATES DIVISION 2

Drawn By: C. PAYNE	Scale: 1" = 100'
Date: 2/14/2024	Project: 22025

Instrument # 1765759 Fully Platted
02/15/2024 02:21:38 PM
Pocatello, Idaho
Global Land Works
S-355
Book 10, Plat 1

Instrument # 1765799
Falls, Idaho
04/16/2024 09:21:38 PM No. of Pages: 2
Recorded for: GLOBAL LAND WORKS
Sherry Manning Fee: \$11.00
Ex-Officio Recorder Deputy
Index to: PLAT
Evega

OWNER'S DEDICATION

KNOW ALL MEN BY THESE PRESENTS: THAT THE UNDERSIGNED HF VENTURES, LLC AN IDAHO LIMITED LIABILITY COMPANY, IS THE LAWFUL OWNER OF THE TRACT OF LAND INCLUDED WITHIN THE BOUNDARY DESCRIPTION SHOWN HEREON AND HAS CAUSED THE SAME TO BE PLATTED AND DIVIDED INTO LOTS, BLOCKS AND STREETS, WHICH PLAT SHALL HEREAFTER BE KNOWN AS SAND CREEK ESTATES DIVISION No. 2, A SUBDIVISION OF THE CITY OF IDAHO FALLS, IDAHO, BONNEVILLE COUNTY, IDAHO.

BE IT FURTHER KNOWN, THAT THE OWNER DOES HEREBY DEDICATE GRANT AND CONVEY TO THE PUBLIC, ALL STREETS AND RIGHT-OF-WAYS SHOWN HEREON, THAT OWNER ALSO DOES HEREBY GRANT AND CONVEY TO THE CITY OF IDAHO FALLS ALL PUBLIC EASEMENTS FOREVER AS IRREVOCABLE PERMANENT NON-EXCLUSIVE PUBLIC EASEMENTS AS SHOWN AND DESCRIBED HEREON.

OWNER, OR ITS HEIRS, SUCCESSORS AND ASSIGNS, AGREE THEY WILL CONSTRUCT NO PERMANENT STRUCTURE WITHIN OR UPON ANY EASEMENT SHOWN HEREON, AND THE CITY OF IDAHO FALLS AND ITS SUCCESSORS, ASSIGNS, PERMITTEES OR LICENSEES SHALL ALSO HAVE THE RIGHT, TO REMOVE, CUT OR TRIM ANY TREES, BRUSH, ORNAMENTAL SHRUBBERY OR PLANT WHICH MAY INJURE OR INTERFERE WITH THE USE THEREOF FOR ITS INTENDED PURPOSES, SUCH RIGHT MAY BE EXERCISED WITHOUT PRIOR NOTICE TO OWNER, OR ITS HEIRS, SUCCESSORS OR ASSIGNS.

OWNER, OR ITS HEIRS, SUCCESSORS OR ASSIGNS FURTHER AGREE THAT THEY SHALL NOT PLANT ANY TREES, BRUSH, ORNAMENTAL SHRUBBERY OR PLANTS WHICH MAY HINDER THE SAFE AND EFFICIENT UTILIZATION OF SAID EASEMENTS.

OWNER, OR ITS HEIRS, SUCCESSORS OR ASSIGNS HEREBY RELEASES THE CITY OF IDAHO FALLS AND ITS SUCCESSORS, ASSIGNS, PERMITTEES OR LICENSEES FROM ANY CLAIM FOR DAMAGES, BASED UPON CONCEALED OR UNDISCLOSED PRIVATE IMPROVEMENTS CONSTRUCTED OR PERMITTED TO BE CONSTRUCTED BY OWNER, OR ITS SUCCESSORS OR ASSIGNS WITHIN ANY PUBLIC EASEMENTS, SUBSEQUENT TO RECORDING THIS SUBDIVISION, THAT MAY BE INCURRED AS A RESULT OF THE CITY OF IDAHO FALLS AND ITS SUCCESSORS, ASSIGNS, PERMITTEES OR LICENSEES ORDINARY USE OF THE PUBLIC EASEMENTS WITH DUE CARE.

OWNER OR ITS HEIRS, SUCCESSORS OR ASSIGNS DO HEREBY WARRANT AND SHALL DEFEND SUCH DEDICATION AND CONVEYANCES IN THE QUIET AND PEACEFUL POSSESSION OF THE PUBLIC OR THE CITY OF IDAHO FALLS, AS THE CASE MAY BE, AGAINST SAID OWNER AND ITS HEIRS, SUCCESSORS AND ASSIGNS, AND AGAINST EVERY PERSON WHOMSOEVER WHO LAWFULLY HOLDS OR WHO LATER CLAIMS TO HAVE LAWFULLY HELD ANY RIGHTS IN SAID ESTATE AS OF THE DATE HEREOF.

IN WITNESS WHEREOF, OWNER HAS HEREUNTO SUBSCRIBED ITS SEALS AND SIGNATURES THIS 29th DAY OF February, 2024.

HF VENTURES, LLC

Brett Falkenrath
BRETT FALKENRATH, MEMBER

Collin Hunter
COLLIN HUNTER, MEMBER

BOUNDARY DESCRIPTION

PART OF THE NORTHWEST QUARTER OF SECTION 4, TOWNSHIP 1 NORTH, RANGE 38 EAST OF THE BOISE MERIDIAN, BONNEVILLE COUNTY, STATE OF IDAHO.

COMMENCING AT WEST CORNER OF SAID SECTION 4 (FROM WHICH THE NORTHWEST CORNER OF SECTION 4 BEARS N 00°02'46" E 2644.04'), THENCE N 00°02'46" E 961.97' ALONG THE WEST LINE OF SECTION 4, THENCE S 89°57'14" E 64.42' TO A POINT ON THE EAST RIGHT-OF-WAY LINE OF 15TH EAST ALSO BEING THE POINT OF BEGINNING;

THENCE N 89°14'03" E 707.06' ALONG THE SOUTH BOUNDARY OF THE LANDS DESCRIBED IN DEED INSTRUMENT No. 1523269;
THENCE N 01°28'32" W 306.00' ALONG THE EAST BOUNDARY OF THE LANDS DESCRIBED IN DEED INSTRUMENT No. 1523269;
THENCE N 88°49'59" E 556.77' ALONG THE SOUTH BOUNDARY OF THE LANDS DESCRIBED IN DEED INSTRUMENT No. 1247752 TO THE WEST BOUNDARY OF THE LANDS DESCRIBED IN DEED INSTRUMENT No. 1535915;
THENCE S 00°06'42" W 699.10' ALONG THE WEST BOUNDARY OF THE LANDS DESCRIBED IN DEED INSTRUMENT No. 1535915 TO THE NORTH BOUNDARY OF SAND CREEK ESTATES DIVISION No. 3 FILED AS INSTRUMENT No. 1723238;
THENCE ALONG THE NORTH BOUNDARY OF SAND CREEK ESTATES DIVISION No. 3 INSTRUMENT No. 1723238 AND SAND CREEK ESTATES DIVISION No. 1 INSTRUMENT No. 1685057 FOR THE FOLLOWING FOUR (4) COURSES:

- 1) S 88°36'07" W 102.42';
- 2) S 88°34'00" W 60.00';
- 3) S 01°26'05" E 19.86';
- 4) N 89°51'57" W 916.52' TO THE EAST BOUNDARY THE LANDS DESCRIBED IN DEED INSTRUMENT No. 1277638;

THENCE N 00°47'47" W 344.95' ALONG THE EAST BOUNDARY THE LANDS DESCRIBED IN DEED INSTRUMENT No. 1277638 TO THE SOUTH BOUNDARY OF THE LANDS DESCRIBED IN DEED INSTRUMENT No. 1744194;

THENCE ALONG THE SOUTH BOUNDARY OF THE LANDS DESCRIBED IN DEED INSTRUMENT No. 1744194 FOR THE FOLLOWING THREE (3) COURSES:

- 1) S 89°12'52" W 140.54';
- 2) S 44°13'23" W 28.29';
- 3) S 89°12'52" W 10.00' TO THE EAST RIGHT-OF-WAY LINE OF 15TH EAST;
- THENCE N 00°46'06" W 71.54' ALONG THE EAST RIGHT-OF-WAY LINE OF 15TH EAST TO THE POINT OF BEGINNING.

SAID PROPERTY CONTAINS 14.088 ACRES MORE OR LESS

ACKNOWLEDGMENT

STATE OF IDAHO
COUNTY OF Bonneville } SS.

ON THIS 22 DAY OF February, 2024, BEFORE ME THE UNDERSIGNED, A NOTARY PUBLIC IN AND FOR SAID STATE, PERSONALLY APPEARED COLLIN HUNTER, KNOWN OR IDENTIFIED TO ME, TO BE A MEMBER OF THE LIMITED LIABILITY COMPANY OF HF VENTURES, LLC AND THE PERSON WHO SUBSCRIBED SAID LIMITED LIABILITY COMPANY'S NAME TO THE FOREGOING OWNER'S DEDICATION, AND THE DRINKING WATER SYSTEM CERTIFICATE AND ACKNOWLEDGED TO ME THAT HE EXECUTED THE SAME IN SAID LIMITED LIABILITY COMPANY'S NAME AS A PERSON AUTHORIZED TO BIND SUCH LIMITED LIABILITY COMPANY.

IN WITNESS WHEREOF, I HAVE HEREUNTO SET MY HAND AND AFFIXED MY OFFICIAL SEAL THE DAY AND THE YEAR IN THIS CERTIFICATE FIRST ABOVE WRITTEN.

NOTARY PUBLIC FOR THE STATE OF IDAHO: Hillary Grover

RESIDING AT: Bingham County

MY COMMISSION EXPIRES ON: 7/13/2029

ACKNOWLEDGMENT

STATE OF IDAHO
COUNTY OF Bonneville } SS.

ON THIS 29th DAY OF February, 2024, BEFORE ME THE UNDERSIGNED, A NOTARY PUBLIC IN AND FOR SAID STATE, PERSONALLY APPEARED BRETT FALKENRATH, KNOWN OR IDENTIFIED TO ME, TO BE A MEMBER OF THE LIMITED LIABILITY COMPANY OF HF VENTURES, LLC AND THE PERSON WHO SUBSCRIBED SAID LIMITED LIABILITY COMPANY'S NAME TO THE FOREGOING OWNER'S DEDICATION, AND THE DRINKING WATER SYSTEM CERTIFICATE AND ACKNOWLEDGED TO ME THAT HE EXECUTED THE SAME IN SAID LIMITED LIABILITY COMPANY'S NAME AS A PERSON AUTHORIZED TO BIND SUCH LIMITED LIABILITY COMPANY.

IN WITNESS WHEREOF, I HAVE HEREUNTO SET MY HAND AND AFFIXED MY OFFICIAL SEAL THE DAY AND THE YEAR IN THIS CERTIFICATE FIRST ABOVE WRITTEN.

NOTARY PUBLIC FOR THE STATE OF IDAHO: Rosalie Ericsson

RESIDING AT: Jefferson County

MY COMMISSION EXPIRES ON: 7/13/2029

TREASURER'S CERTIFICATE

I, THE UNDERSIGNED COUNTY TREASURER IN AND FOR THE COUNTY OF BONNEVILLE, STATE OF IDAHO, PURSUANT TO THE REQUIREMENTS OF I.C. §50-1308, DO HEREBY CERTIFY THAT ALL COUNTY PROPERTY TAXES DUE FOR THE PROPERTY INCLUDED IN THE BOUNDARY DESCRIPTION SHOWN HEREON ARE CURRENT.

Craig H. Tibbitts by DA
BONNEVILLE COUNTY TREASURER

RECORDER'S CERTIFICATE

I HEREBY CERTIFY THAT THE FOREGOING PLAT OF SAND CREEK ESTATES DIVISION No. 2, WAS FILED IN THE OFFICE OF THE RECORDER OF BONNEVILLE COUNTY, IDAHO

Devin Saxton
BONNEVILLE COUNTY RECORDER

Instrument # 1765799
Falls, Idaho
04/16/2024 09:21:38 PM No. of Pages: 2
Recorded for: GLOBAL LAND WORKS
Sherry Manning Fee: \$11.00
Ex-Officio Recorder Deputy
Index to: PLAT
Evega

HEALTH DEPARTMENT CERTIFICATE OF APPROVAL

SANITARY RESTRICTIONS AS REQUIRED BY I.C. §50-1326 HAVE BEEN SATISFIED BASED ON THE DEPARTMENT OF ENVIRONMENTAL QUALITY (DEQ) APPROVAL OF THE DESIGN PLANS AND SPECIFICATIONS AND THE CONDITIONS IMPOSED ON THE DEVELOPER FOR CONTINUED SATISFACTION OF THE SANITARY RESTRICTIONS. BUYER IS CAUTIONED THAT AT THE TIME OF THIS APPROVAL, NO DRINKING WATER OR SEWER/SEPTIC FACILITIES HAVE BEEN CONSTRUCTED. BUILDING CONSTRUCTION CAN BE ALLOWED WITH THE APPROPRIATE BUILDING PERMITS IF DRINKING WATER OR SEWER FACILITIES HAVE SINCE BEEN CONSTRUCTED OR IF THE DEVELOPER IS SIMULTANEOUSLY CONSTRUCTING THOSE FACILITIES. IF THE DEVELOPER FAILS TO CONSTRUCT FACILITIES OR MEET THE OTHER CONDITIONS OF DEQ, THEN SANITARY RESTRICTIONS MAY BE IMPOSED, IN ACCORDANCE WITH I.C. §50-1326, BY THE ISSUANCE OF A CERTIFICATE OF DISAPPROVAL, AND NO CONSTRUCTION OF ANY BUILDING OR SHELTER REQUIRING DRINKING WATER OR SEWER/SEPTIC FACILITIES SHALL BE ALLOWED.

EASTERN IDAHO PUBLIC HEALTH DEPARTMENT

Michael E. Smith
ENVIRONMENTAL HEALTH SPECIALIST

HILLORY GROVER
COMMISSION NO. 20232919
NOTARY PUBLIC
STATE OF IDAHO
MY COMMISSION EXPIRES 7/13/2029

SAND CREEK ESTATES DIVISION No. 2

A SUBDIVISION OF THE CITY OF IDAHO FALLS, BONNEVILLE COUNTY, IDAHO
BEING PART OF THE NORTHWEST 1/4 OF SECTION 4,
TOWNSHIP 1 NORTH, RANGE 38 EAST OF THE BOISE MERIDIAN

DRINKING WATER SYSTEM CERTIFICATE

PURSUANT TO I.C. §50-1334, THE OWNER DOES HEREBY CERTIFY THAT ALL LOTS SHOWN ON THIS PLAT ARE ELIGIBLE TO RECEIVE WATER FROM THE CITY OF IDAHO FALLS MUNICIPAL WATER SYSTEM AND SAID CITY HAS AGREED IN WRITING TO PROVIDE CULINARY WATER SERVICE TO SAID LOTS PURSUANT TO THE PROVISIONS OF TITLE 8, CHAPTER 4 OF THE IDAHO FALLS CITY CODE AS AMENDED FROM TIME TO TIME.

IN WITNESS WHEREOF, OWNER HAS HEREUNTO SET ITS SIGNATURES THIS 29th DAY OF February, 2024.

HF VENTURES, LLC

Brett Falkenrath
BRETT FALKENRATH, MEMBER

Collin Hunter
COLLIN HUNTER, MEMBER

IRRIGATION WATER RIGHTS STATEMENT

THE PROPERTY INCLUDED IN THIS PLAT HAS PETITIONED FOR AND HAS BEEN REMOVED FROM ALL FUTURE IRRIGATION WATER RIGHTS.

DATE: 02/11/2021

INSTRUMENT No. 1674924

FLOOD PLAIN DESIGNATION

ZONE X PER FLOOD INSURANCE RATE MAP COMMUNITY-PANEL NUMBER 1600270235 D, EFFECTIVE DATE APRIL 2, 2002.

CITY'S ACCEPTANCE

THE ACCOMPANYING PLAT WAS DULY ACCEPTED AND APPROVED AND THE GRANTS AND DEDICATIONS ARE HEREBY ACCEPTED BY THE CITY COUNCIL OF IDAHO FALLS ADOPTED THIS 8th DAY OF February, 2024.

Rosalie Ericsson
MAYOR

Craig Tibbitts
CITY CLERK

Kent J. Fugal
CITY ENGINEER
KENT J. FUGAL, PE 9247

Kenneth Baldwin Roberts
CITY SURVEYOR
KENNETH BALDWIN ROBERTS, PLS 9755

COUNTY SURVEYOR'S VERIFICATION

I CERTIFY THAT I AM A LICENSED PROFESSIONAL LAND SURVEYOR IN THE STATE OF IDAHO AND THAT I HAVE EXAMINED THIS PLAT AND FIND THAT IT COMPLIES WITH I.C. §50-1305.


David D. Romrell
BONNEVILLE COUNTY SURVEYOR, DAVID D. ROMRELL, PLS 12223

3/4/2024
DATE

SURVEYOR'S CERTIFICATE

I, CARDON T. PAYNE, A LICENSED PROFESSIONAL LAND SURVEYOR IN THE STATE OF IDAHO, DO HEREBY CERTIFY THAT THE SURVEY OF THIS SUBDIVISION, DESIGNATED AS SAND CREEK ESTATES DIVISION No. 2, WAS MADE UNDER MY DIRECTION, AND THAT SAID SUBDIVISION IS TRULY AND CORRECTLY SURVEYED AND STAKED AS PROVIDED BY LAW AND IN ACCORDANCE WITH THE ACCOMPANYING PLAT AS DESCRIBED HEREON.

CARDON T. PAYNE, PLS 18405

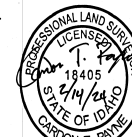

1823 East Center Street, Pocatello, Idaho 83201 Phone: 208.242.8753
globalandworks@gmail.com globalandworks.com

SAND CREEK ESTATES DIVISION 2

Drawn By: C. PAYNE Scale: 1" = 100'
Date: 2/14/2024 Project: 22025